
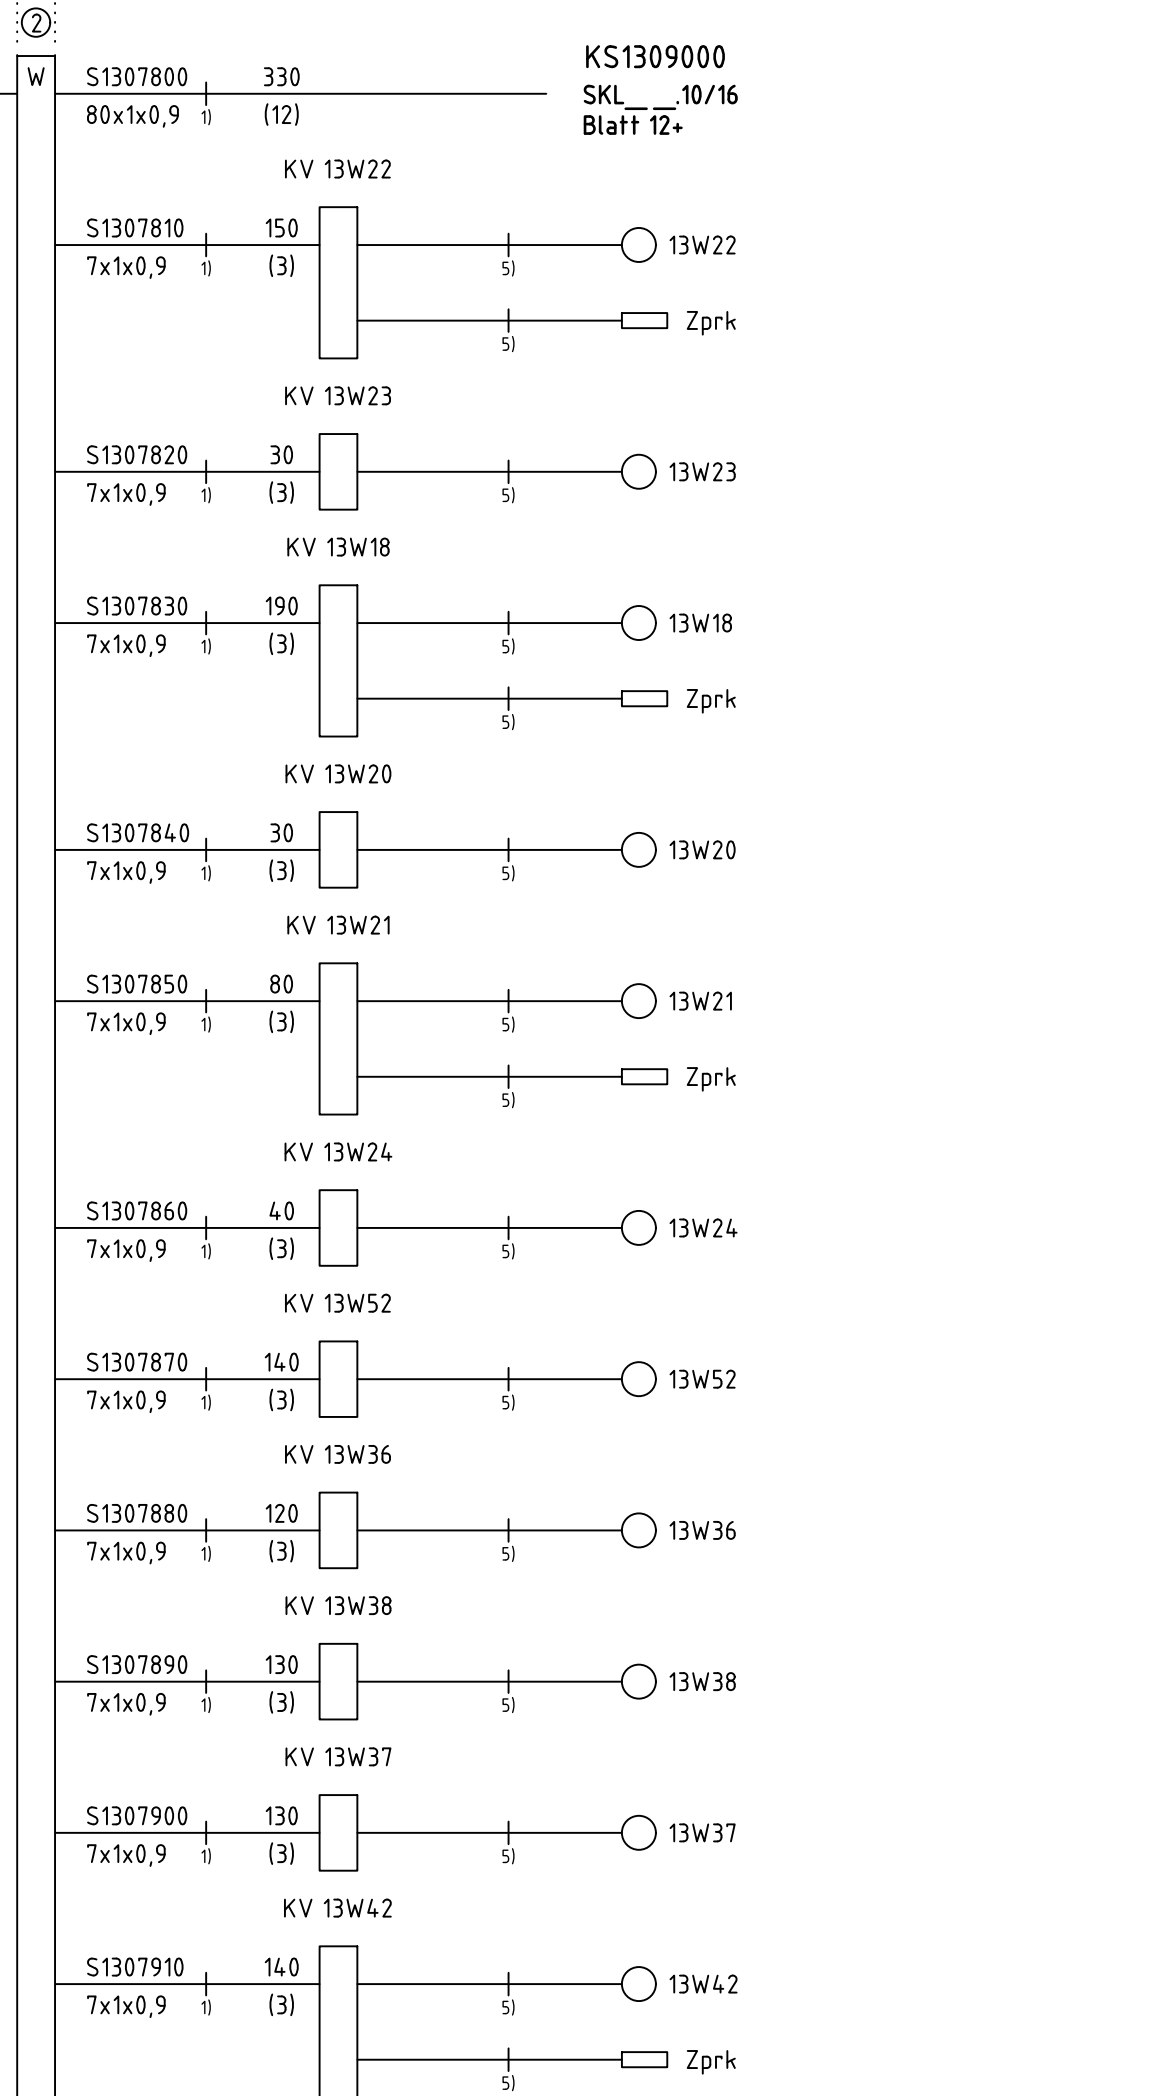
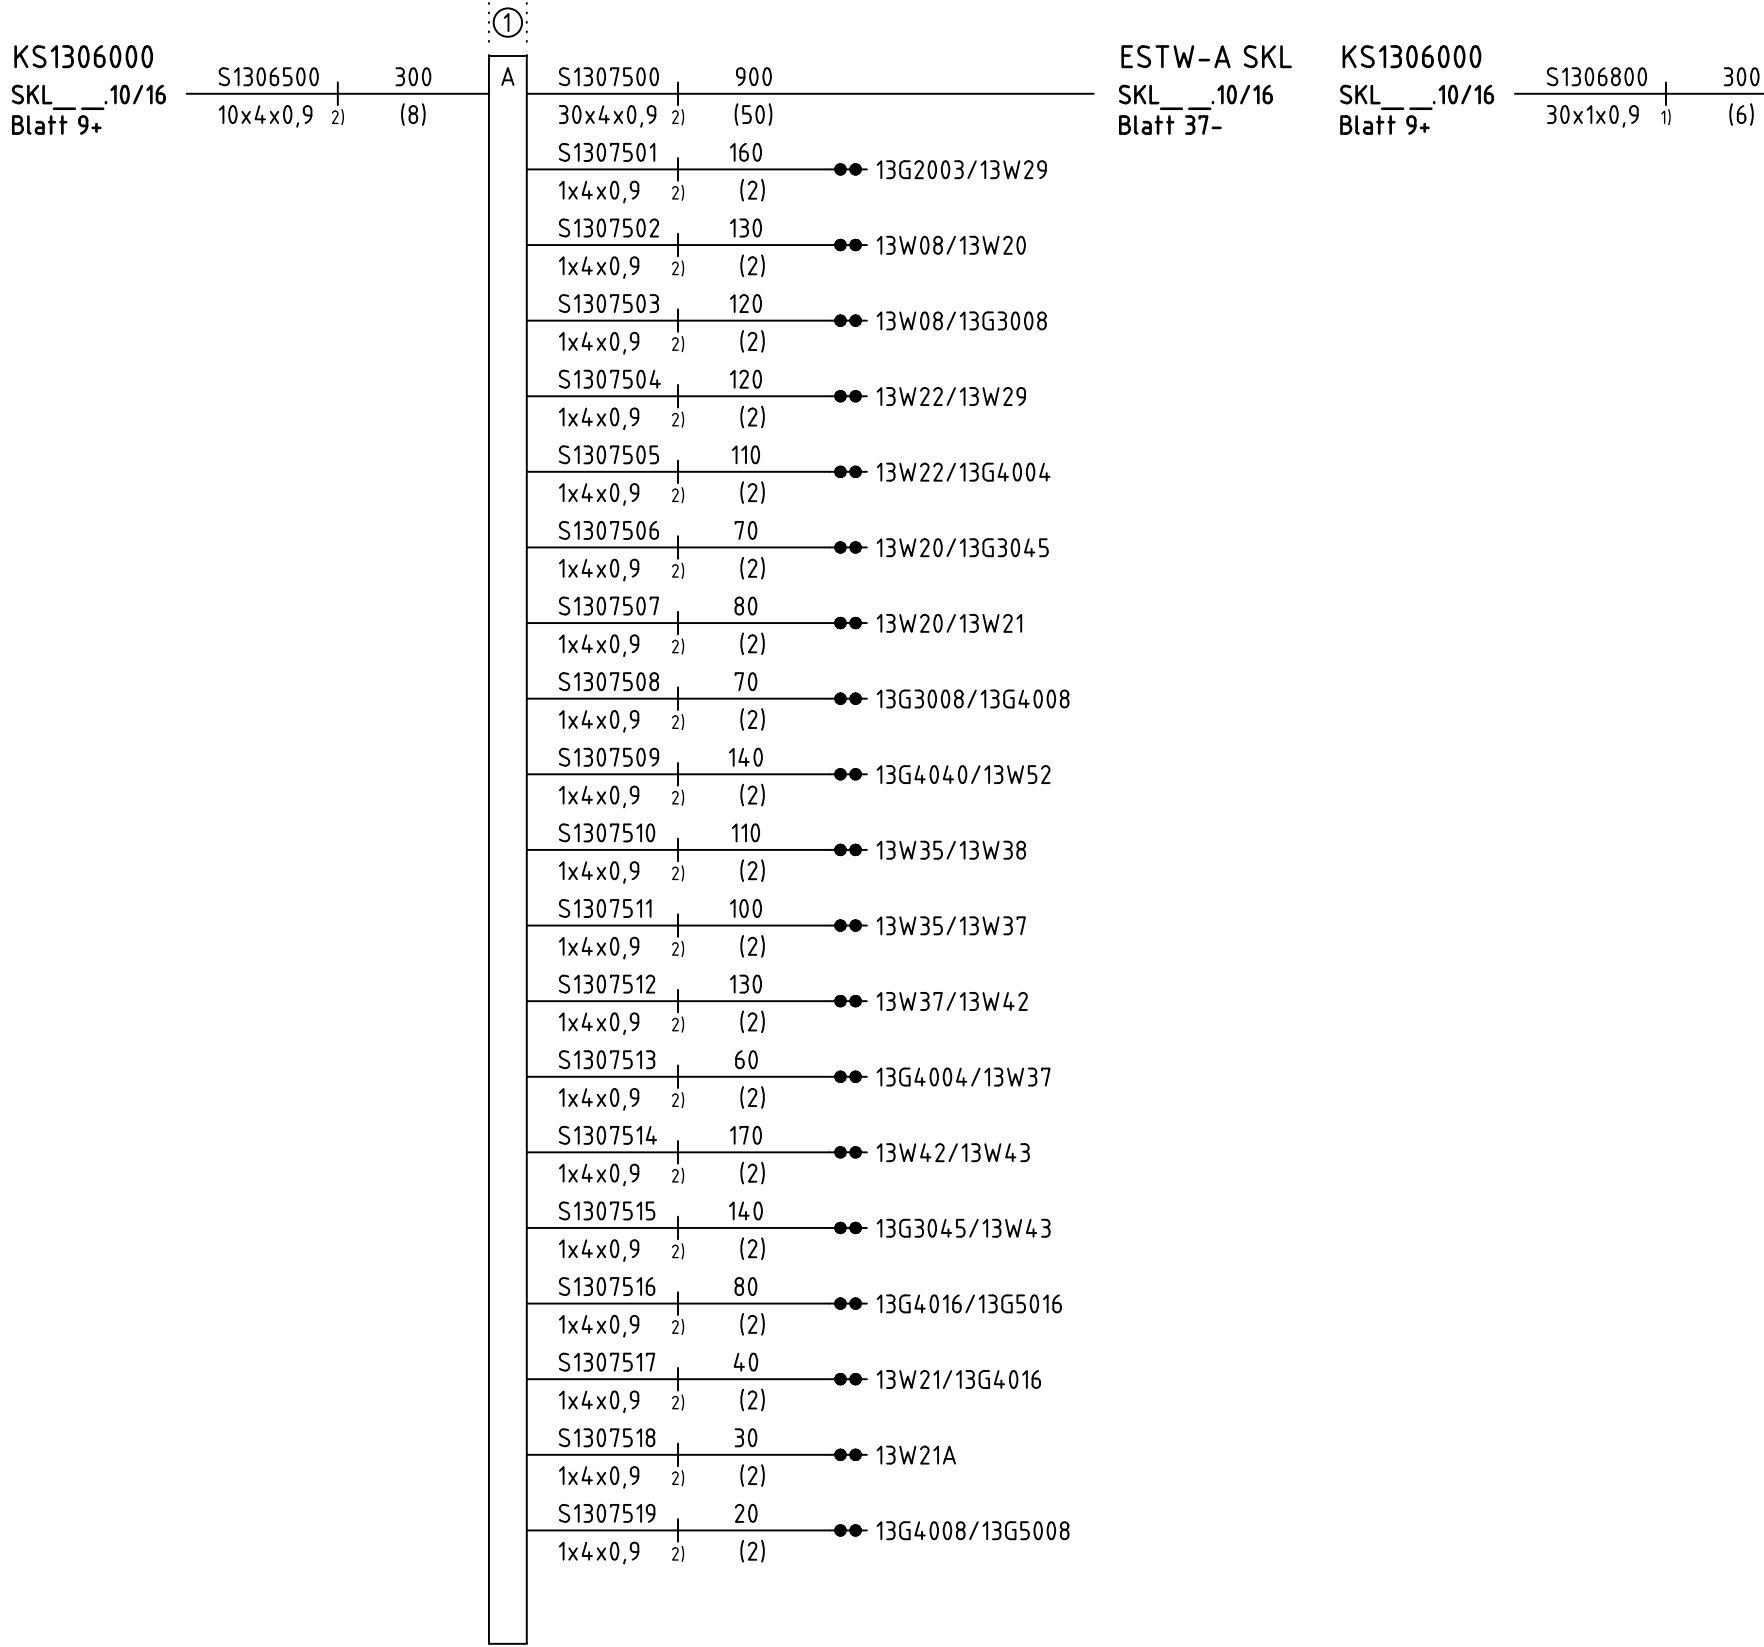


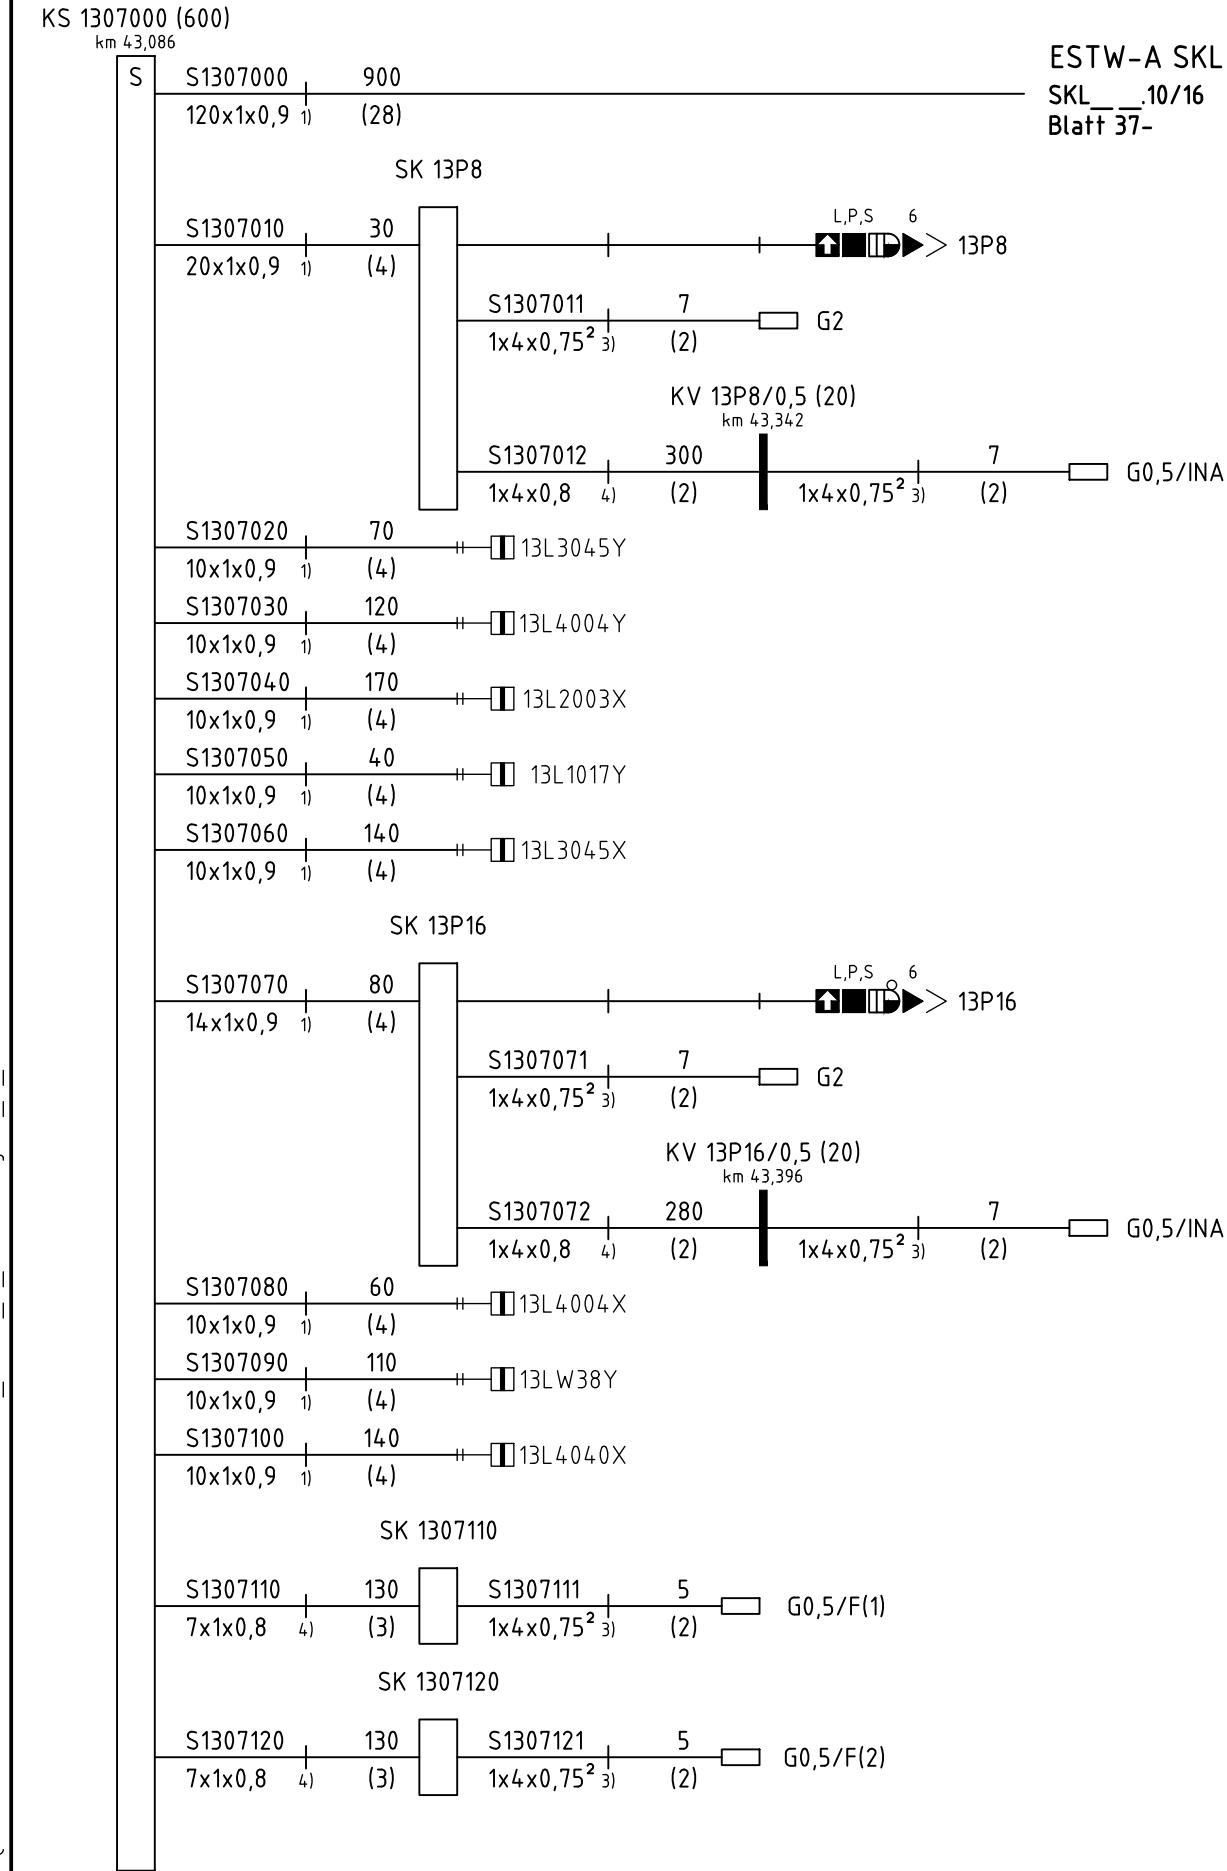

Neubau ESTW Landstuhl, Kaiserslautern und Hochspeyer
im Rahmen POS Nord
Inbetriebnahme

Gleichstellung	Genehmigung zur Bauausführung
Planprüfung	Freigabe der Ausführungsunterlagen (BVB)
